



Republika e Kosovës
Republika Kosova-Republic of Kosova
Qeveria -Vlada-Government

Ministria e Mjedisit dhe Planifikimit Hapësinor /Ministarstvo Sredine i Prostornog Planiranja/Ministry of Environment and Spatial Planning
AGJENCIA KADASTRALE E KOSOVËS/ KATASTARSKA AGENCIJA KOSOVA/ KOSOVA CADASTRAL AGENCY

Zyra kadastrale komunale / Opštinska katastarska kancelarija: Ferizaj

Nr. i njësisë kadastrale / Br. katastarske jedinice : 00433-0
163/2026


Zona kadastrale / Katastarska zona: Mirosalë

Numri i lëndës / Broj predmeta: 186/1172-140/26

Lloji i njësisë kadastrale / Vrsta katastarske jedinice : Parcel

Shkalla e zvoglimit / Razmera plana : 1:500

Nr	Y	X	H	Kodi	Përshkrimi	Burimi
220086M	7512362.413	4694374.649	620.681	11	Monoment	PM
1	7519533.026	4695411.820	632.590	2	Kunjë - shtyllë metalik	PM
2	7519521.580	4695417.864	634.399	2	Kunjë - shtyllë metalik	PM
3	7519512.918	4695422.509	635.491	2	Kunjë - shtyllë metalik	PM
4	7519519.458	4695432.632	635.209	2	Kunjë - shtyllë metalik	PM
6	7519523.329	4695429.784	635.100	2	Kunjë - shtyllë metalik	PM
5	7519524.034	4695430.827	634.993	2	Kunjë - shtyllë metalik	PM
2497	7519531.756	4695448.493	634.436	2	Kunjë - shtyllë metalik	PM
2498	7519494.736	4695462.314	637.909	2	Kunjë - shtyllë metalik	PM
2499	7519486.765	4695436.705	638.103	2	Kunjë - shtyllë metalik	PM
2500	7519481.674	4695418.926	638.352	2	Kunjë - shtyllë metalik	PM
10246	7519510.564	4695418.175	636.007	2	Kunjë - shtyllë metalik	PM
10247	7519521.594	4695407.445	634.869	2	Kunjë - shtyllë metalik	PM
10248	7519528.884	4695402.765	632.477	2	Kunjë - shtyllë metalik	PM
10251	7519523.275	4695436.204	635.058	2	Kunjë - shtyllë metalik	PM
10252	7519524.335	4695428.694	634.827	2	Kunjë - shtyllë metalik	PM
10253	7519537.085	4695420.694	632.857	2	Kunjë - shtyllë metalik	PM

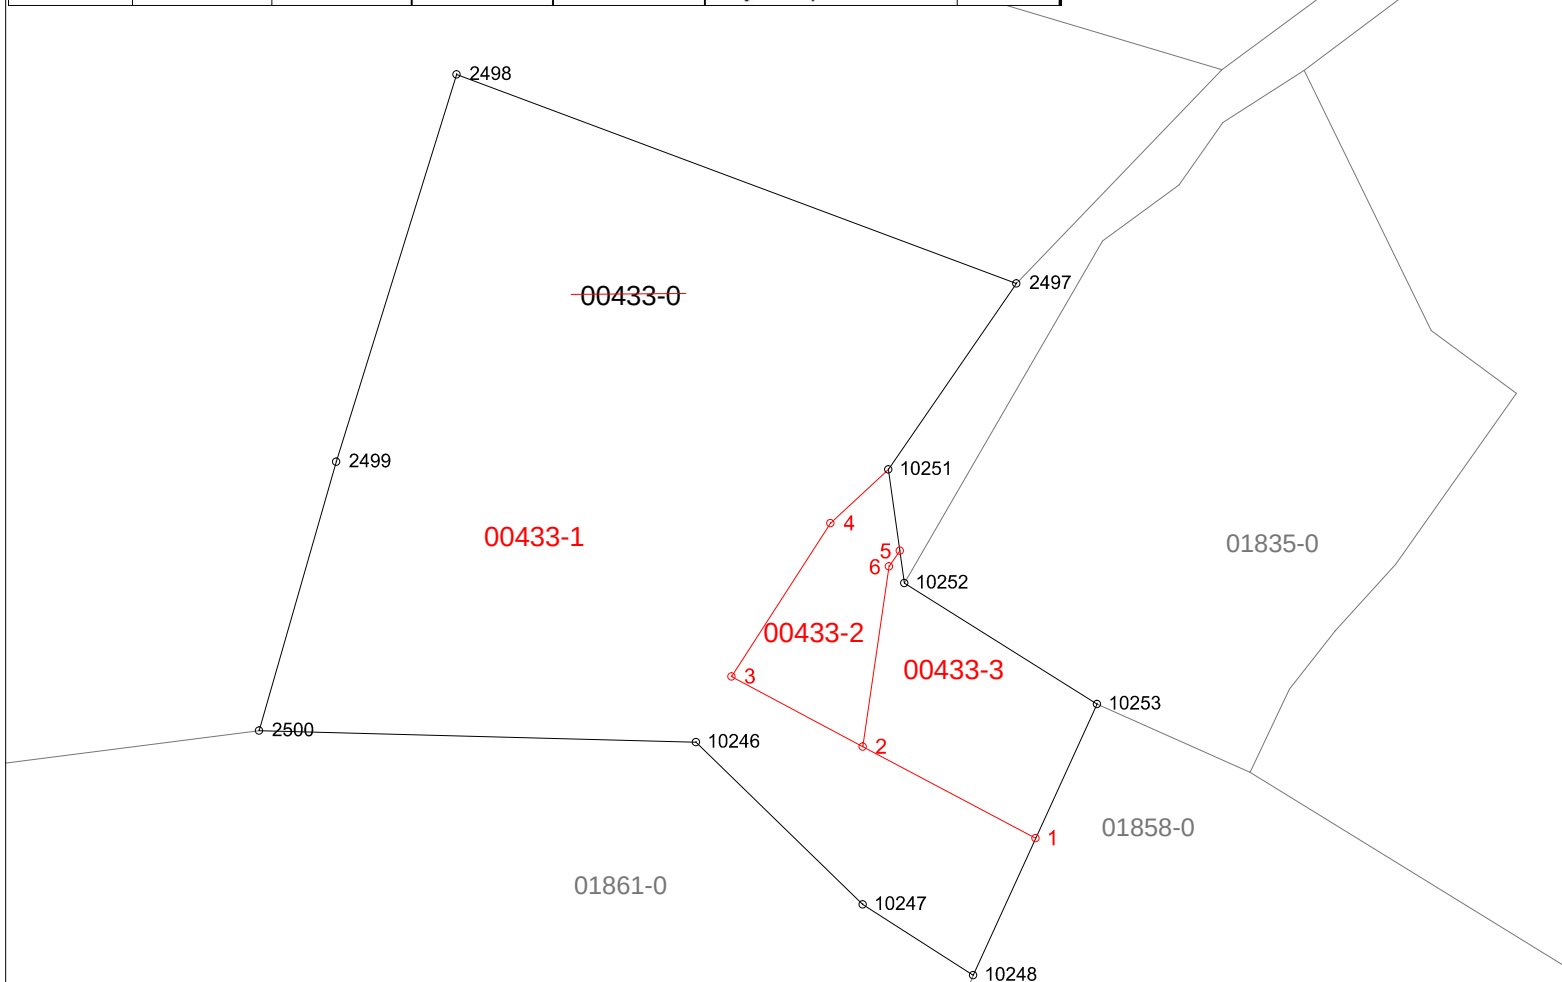

Rilevoi / Snimio: LIRIDON SEJDIU
(emri dhe mbiemri i gjeodetit/kompanisë/ ime i prezime geodeta/ kompanije)

Aprovoi / Usvojio: _____
(emri dhe mbiemri i përsorit zyrtar/ ime i prezime sluzbenog lica)

Nr. i licencës / Br. licence: 140

V.V.

Nënshkrimi / Potpis: _____

Nënshkrimi / Potpis: _____

Data e rilevimit / Datum snimanja: 17.07.2026

Data e aprovimit / Datum usvajanja: _____